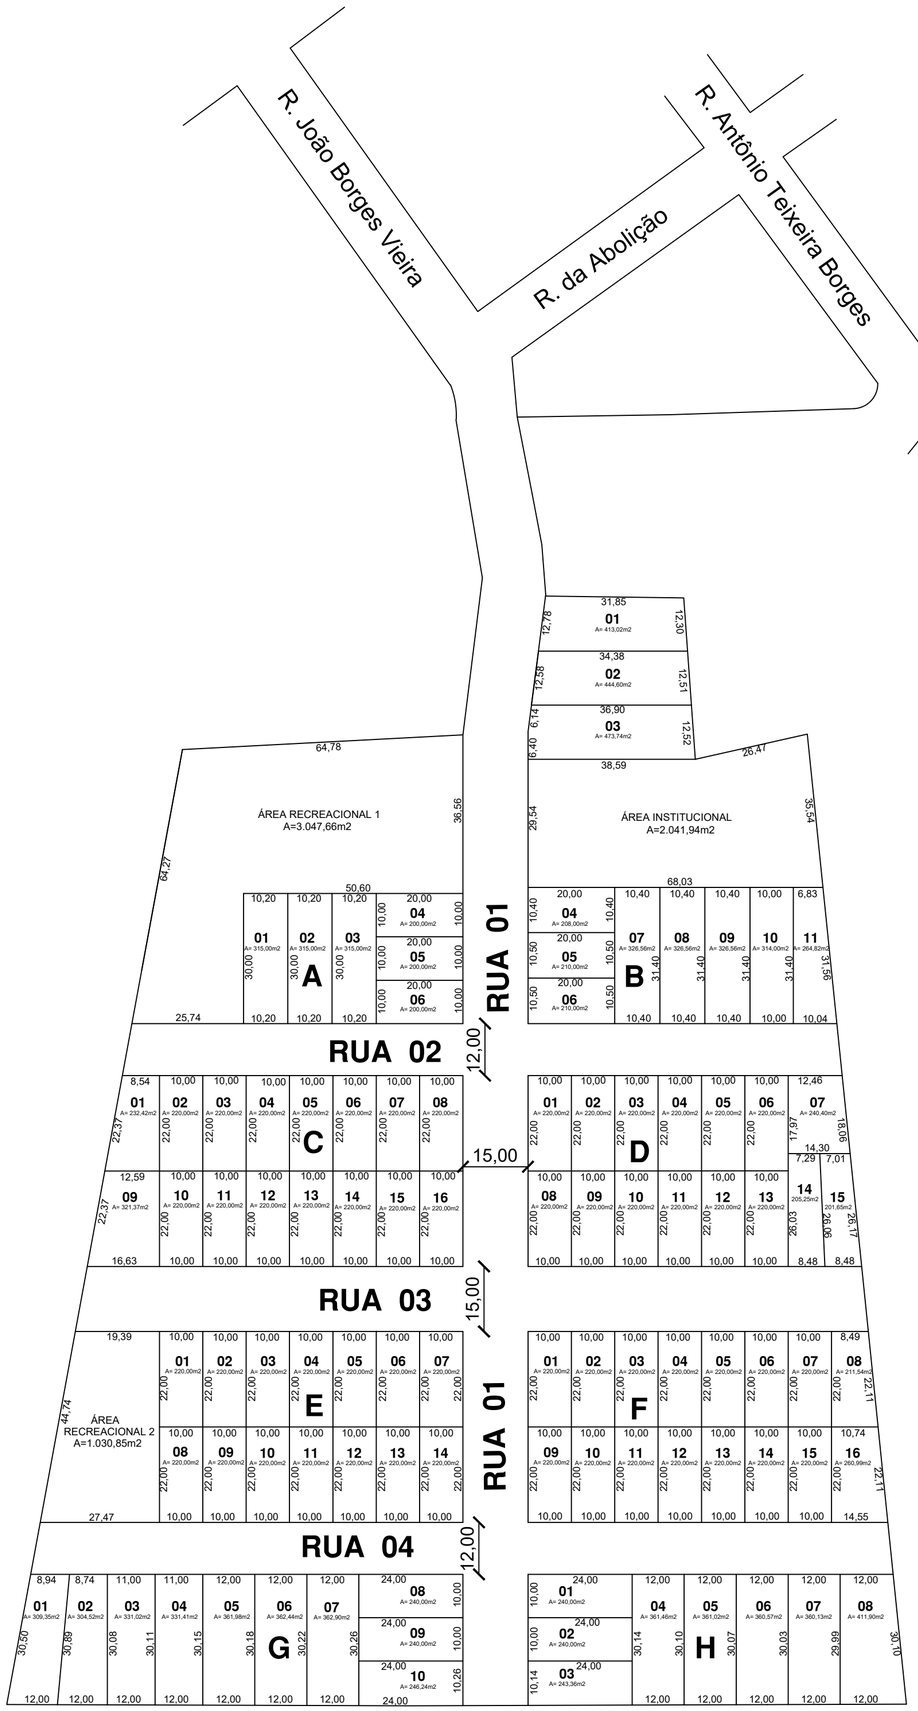


SINTESE QUADRO DE ÁREAS LOTEAMENTO PRIORITÀ

QUADRA A		QUADRA B		QUADRA C		QUADRA D		QUADRA E		QUADRA F		QUADRA G		QUADRA H	
LOTE	ÁREA	LOTE	ÁREA	LOTE	ÁREA	LOTE	ÁREA	LOTE	ÁREA	LOTE	ÁREA	LOTE	ÁREA	LOTE	ÁREA
1	315,00	1	413,02	1	232,42	1	220,00	1	220,00	1	220,00	1	309,35	1	240,00
2	315,00	2	444,60	2	220,00	2	220,00	2	220,00	2	220,00	2	304,52	2	240,00
3	315,00	3	473,74	3	220,00	3	220,00	3	220,00	3	220,00	3	331,02	3	243,36
4	200,00	4	208,00	4	220,00	4	220,00	4	220,00	4	220,00	4	331,41	4	361,46
5	200,00	5	210,00	5	220,00	5	220,00	5	220,00	5	220,00	5	361,98	5	361,02
6	200,00	6	210,00	6	220,00	6	220,00	6	220,00	6	220,00	6	362,44	6	360,57
		7	326,56	7	220,00	7	240,40	7	220,00	7	220,00	7	362,90	7	360,13
SUB-TOTAL	**1545,00**	8	326,56	8	220,00	8	220,00	8	220,00	8	220,00	8	240,00	8	411,90
		9	326,56	9	321,37	9	220,00	9	220,00	9	220,00	9	240,00		
Áreas Município		10	314,00	10	220,00	10	220,00	10	220,00	10	220,00	10	246,24	**TOTAL**	**2578,44**
Recreacional 1	3047,66	11	264,82	11	220,00	11	220,00	11	220,00	11	220,00				
SUB-TOTAL	**3047,66**			12	220,00	12	220,00	12	220,00	12	220,00	**TOTAL**	**3089,86**		
		SUB-TOTAL	**3517,86**	13	220,00	13	220,00	13	220,00	13	220,00				
TOTAL	**4592,66**			14	220,00	14	205,25	14	220,00	14	220,00				
		Áreas Município		15	220,00	15	201,65			15	220,00				
		Institucional	2041,94	16	220,00			**SUB-TOTAL**	**3080,00**	16	260,99				
		SUB-TOTAL	**2041,94**			**TOTAL**	**3287,30**								
				TOTAL	**3633,79**			Áreas Município		**TOTAL**	**3552,53**				
		TOTAL	**5559,80**					Recreacional 2	1030,85						
								SUB-TOTAL	**1030,85**						
								TOTAL	**4110,85**						

RESUMO		
ÁREAS MUNICÍPIO		
	ÁREA (m²)	
RECREACIONAL 1	3047,66	7,48%
RECREACIONAL 2	1030,85	2,54%
INTITUCIONAL	2041,94	5,01%
TOTAL	**6120,45**	
RUAS		
	ÁREA (m²)	
RUA 001	3846,19	
RUA 002	1791,5	
RUA 003	2485,99	
RUA 004	2186,09	
TOTAL	**10309,77**	

SÍNTESE		
QUADRA	**ÁREA (m²)**	**%**
A	1545,00	
B	3517,86	
C	3633,79	
D	3287,30	
E	3080,00	
F	3552,53	
G	3089,86	
H	2578,44	
SUB TOTA	24284,78	59,65%
A. MUNIC.	6120,45	15,03%
A. RUAS	10309,77	25,32%
TOTAL	**40715,00**	**100%**

DOMINGUES
ENGENHARIA CIVIL

Assunto: Projeto Urbanístico		LOCAL: Vacaria / RS	PRANCHA: 01
Área do Terreno 4,0175 ha	ESCALA: 1:1000	DATA: 07/2024	

RESPONSÁVEL TÉCNICO:
GUSTAVO LOPES DOMINGUES:01360588094
Assinado de forma digital por GUSTAVO LOPES DOMINGUES:01360588094
Dados: 2024.09.16 14:15:57 -03'00'

Eng. Civil Gustavo Lopes Domingues
CREA/SC 172315-1

PROPRIETÁRIO:

Fernando Lisboa Priori
CPF: 012.861.580-01